


SCHIȚA CLĂDIRII LIT. „B”

Nivelul P

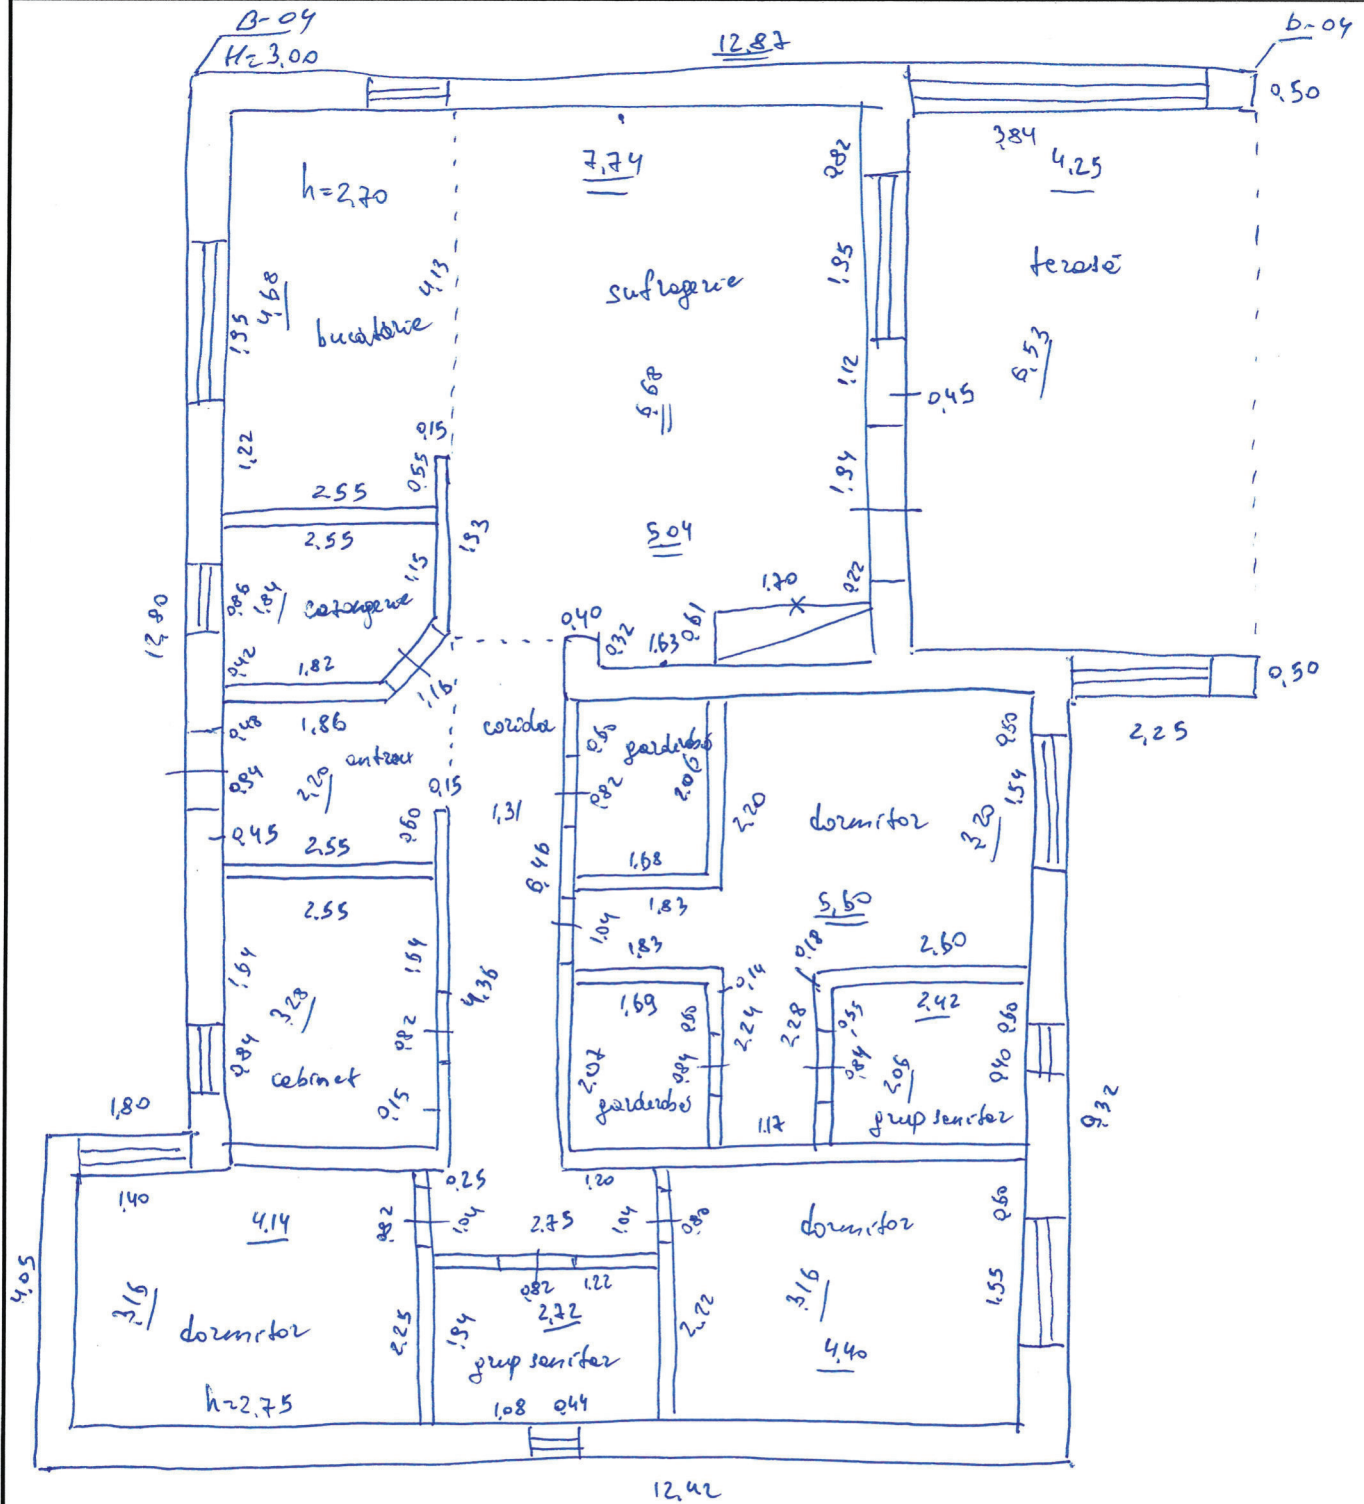

Mențiuni: Autozete Nr 1922 din 29.01.2025

A executat: Luchianenco N.

Data: „02” 03 2026

Verificator: Luchianenco N.

Semnătura beneficiarului:

Data: „02” 03 2026